


NOTES

Do not scale from this drawing, use figured dimensions only.
Notify Project Manager of any discrepancies.
This drawing is to be read in conjunction with all other contract documents and drawings.
This drawing is subject to confirmation by site survey.

ALL CONSTRUCTION MUST BE EXACTLY AS ILLUSTRATED BY THE DRAWINGS. ANY DEPARTURE (EVEN THE SLIGHTEST) FROM THESE DRAWINGS, WILL BE RESPONSIBLE FOR ALL RESULTANT FINANCIAL CONSEQUENCES AND POSSIBLE DISCIPLINARY ACTION.

LEGEND

- Fire escape route
- Fire door - single
- Fire door - double
- Vision panel on door
- Line of compartmentation
- ILLUMINATED emergency fire exit
- Emergency fire exit (running man)
- Emergency lighting
- Manual call point
- Optical beam detector
- Fire panel
- Beam light (emergency)
- Fire alarm sounder
- Flashing beacon
- Sounder with beacon
- Smoke detector
- Smoke detector with sounder base
- Smoke detector with sounder and beacon
- Smoke detector in void
- Smart 3 detector
- Smart 3 detector with sounder base
- Smart 3 detector with sounder and beacon
- Heat detector
- Heat detector with sounder base
- Heat detector with sounder and beacon
- Heat detector in void
- FIRE FIGHTING EQUIPMENT
- Refuge point
- Fire Hydrant
- Water fire extinguisher
- Carbon dioxide fire extinguisher (or halon)
- Foam fire extinguisher
- Dry powder extinguisher
- Fire extinguisher wet chemical
- Aqueous film forming foam extinguisher
- Fire blanket in container
- Sand bucket

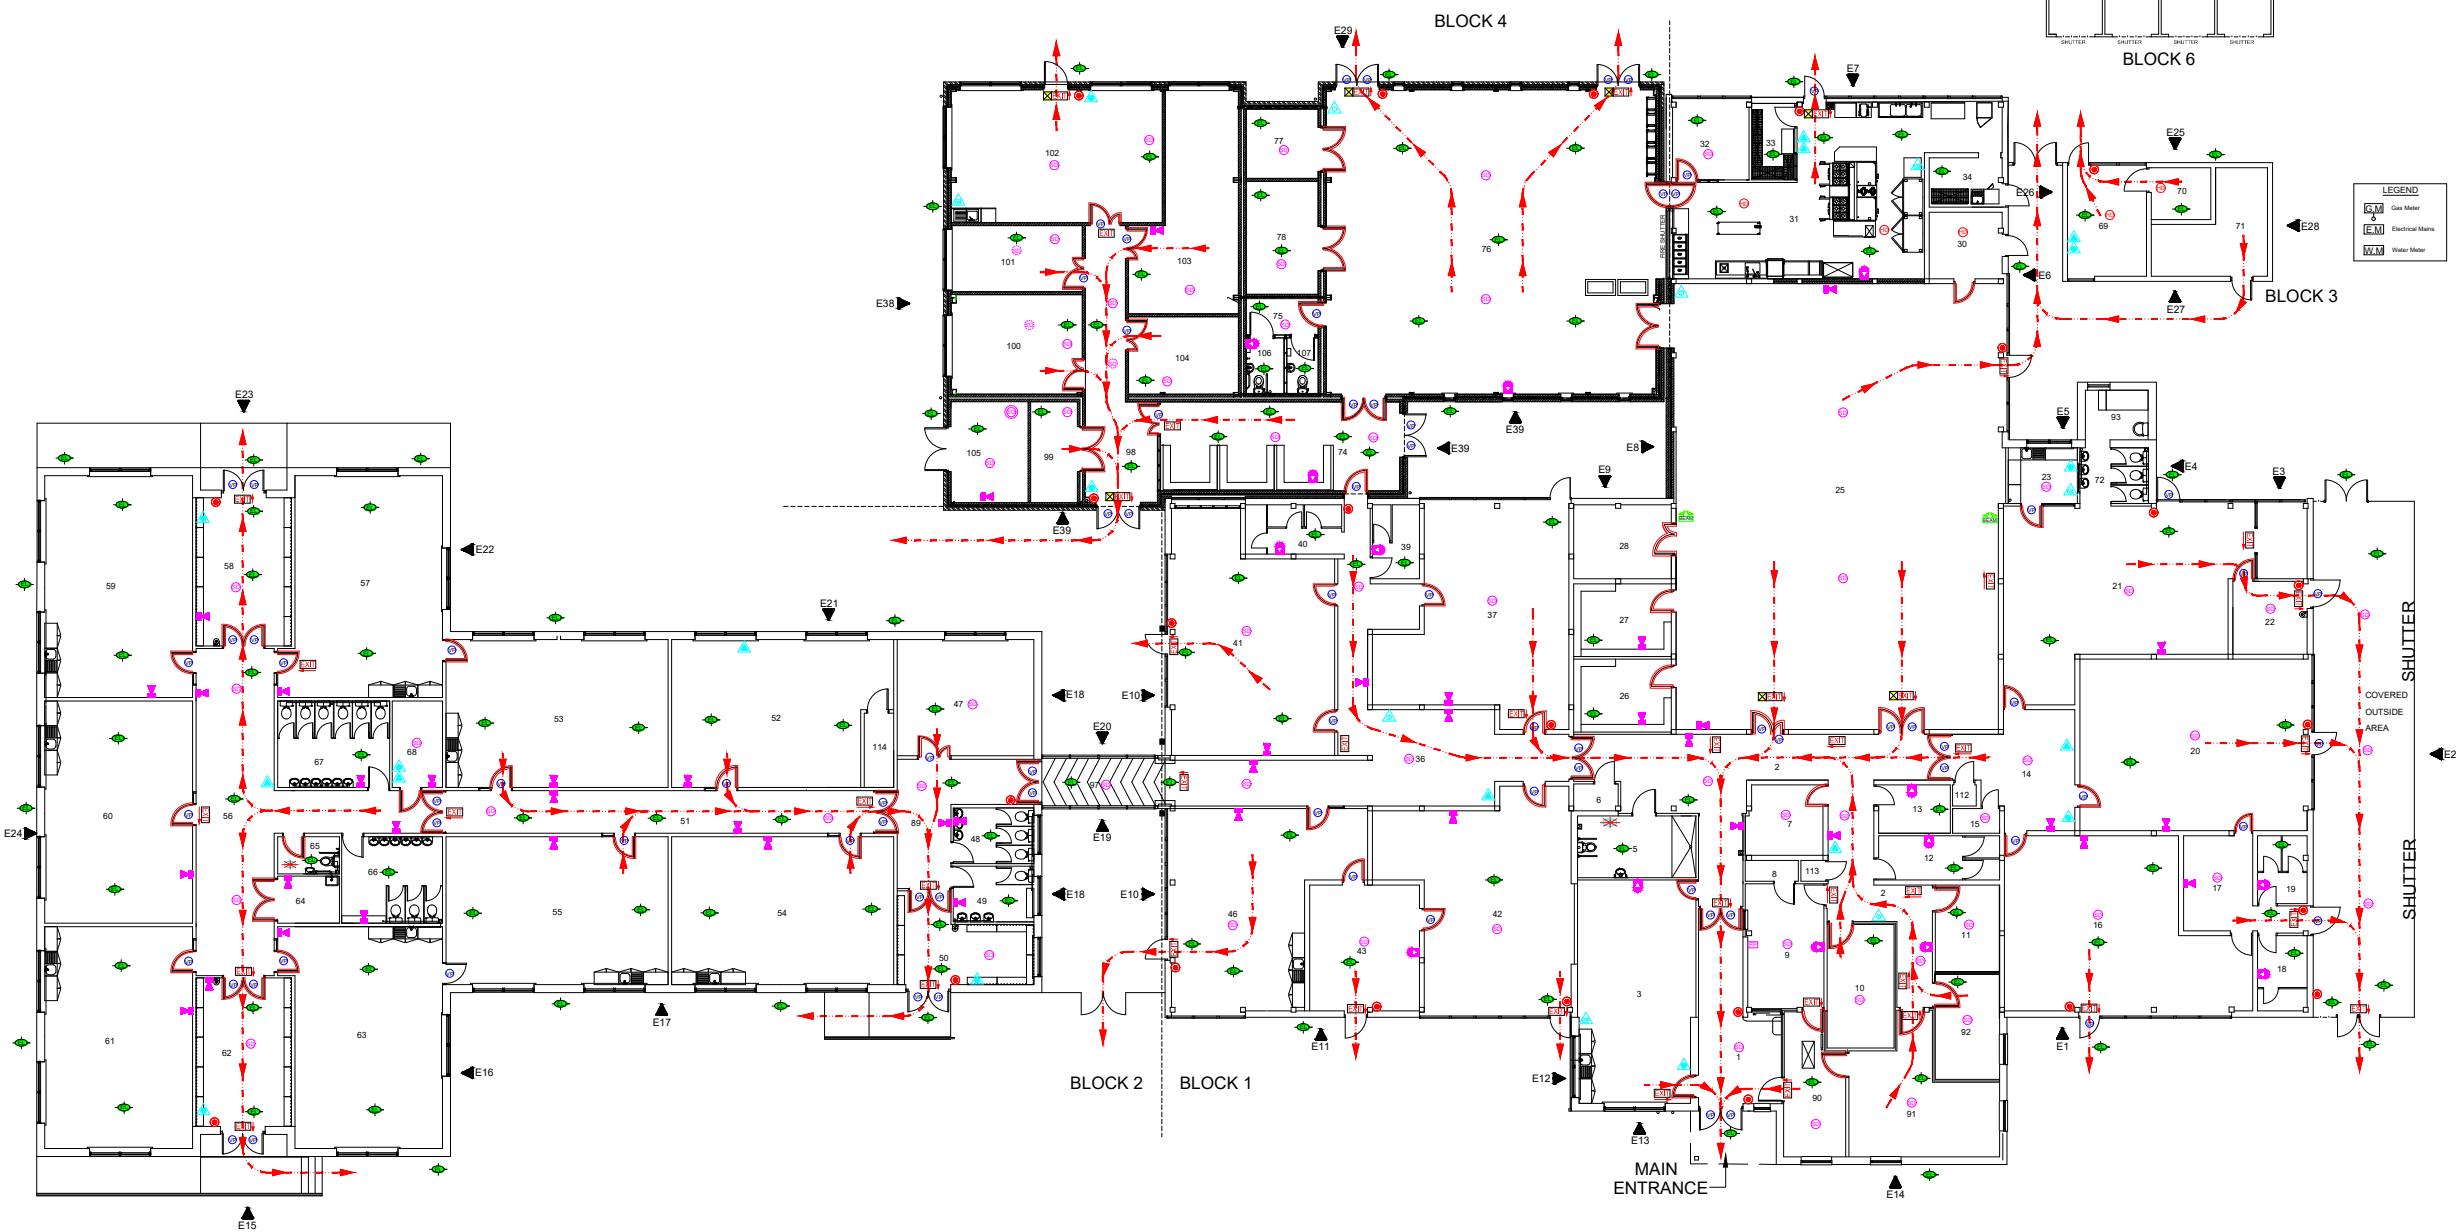

Ground Floor

Water meter at entrance
Gas meter at entrance

DATE	REV	REVISION DESCRIPTION	REV BY
City of Bradford Metropolitan District Council			
www.bradford.gov.uk			
Department of Corporate Services			
Building & Technical Services			
Assistant Director - Ben Middleton			
3rd Floor, Delamare House, Hall Ings, Bradford, BD1 1HX. Tel: (01274) 431877			
CLIENT			
EDUCATION			
PROJECT			
GROVE HOUSE PRIMARY SCHOOL			
DRAWING			
FIRE PREVENTION STRATEGY			
FLOOR PLANS			
PROJECT MANAGER		OS REF	
T.C		*****/*****	
DRAWN BY	DATE	APPROVED	SCALE
MAW	14/04/2021	WS	NTS
DRAWING No.		REVISION No.	
11/02093/2/6/0/01			

NOTES

Do not scale from this drawing, use figured dimensions only.
Notify Project Manager of any discrepancies.
This drawing is to be read in conjunction with all other contract documents and drawings.
This drawing is subject to confirmation by site survey.

ALL CONSTRUCTION MUST BE EXACTLY AS ILLUSTRATED BY THE DRAWINGS. ANY DEPARTURE (EVEN THE SLIGHTEST) FROM THESE DRAWINGS, WILL BE RESPONSIBLE FOR ALL RESULTANT FINANCIAL CONSEQUENCES AND POSSIBLE DISCIPLINARY ACTION.

LEGEND

- Fire escape route
- Fire door - single
- Fire door - double
- Vision panel on door
- Line of compartmentation
- ILLUMINATED emergency fire exit
- Emergency fire exit (running man)
- Emergency lighting
- Manual call point
- Optical beam detector
- Fire panel
- Beam light (emergency)
- Fire alarm sounder
- Flashing beacon
- Sounder with beacon
- Smoke detector
- Smoke detector with sounder base
- Smoke detector with sounder and beacon
- Smoke detector in void
- Smart 3 detector
- Smart 3 detector with sounder base
- Smart 3 detector with sounder and beacon
- Heat detector
- Heat detector with sounder base
- Heat detector with sounder and beacon
- Heat detector in void
- FIRE FIGHTING EQUIPMENT
- Refuge point
- Fire Hydrant
- Water fire extinguisher
- Carbon dioxide fire extinguisher (or halon)
- Foam fire extinguisher
- Dry powder extinguisher
- Fire extinguisher wet chemical
- Aqueous film forming foam extinguisher
- Fire blanket in container
- Sand bucket

2017 Building

BLOCK 4

BLOCK 6

BLOCK 3

BLOCK 2

BLOCK 1

MAIN ENTRANCE

2001 Building

Ground Floor

Water meter at entrance
Gas meter at entrance

DATE	REV	REVISION DESCRIPTION	REV BY
City of Bradford Metropolitan District Council			
www.bradford.gov.uk			
Department of Corporate Services			
Building & Technical Services			
Assistant Director - Ben Middleton			
3rd Floor, Delamare House, Hall Ings, Bradford, BD1 1HX. Tel: (01274) 431877			
CLIENT			
EDUCATION			
PROJECT			
GROVE HOUSE PRIMARY SCHOOL			
DRAWING			
FIRE PREVENTION STRATEGY			
FLOOR PLANS			
PROJECT MANAGER		OS REF	
T.C		*****/*****	
DRAWN BY	DATE	APPROVED	SCALE
MAW	14/04/2021	WS	NTS
DRAWING No.		REVISION No.	
11/02093/2/6/0/01			